


SƠ ĐỒ TỔ CHỨC KHÔNG GIAN KIẾN TRÚC CẢNH QUAN

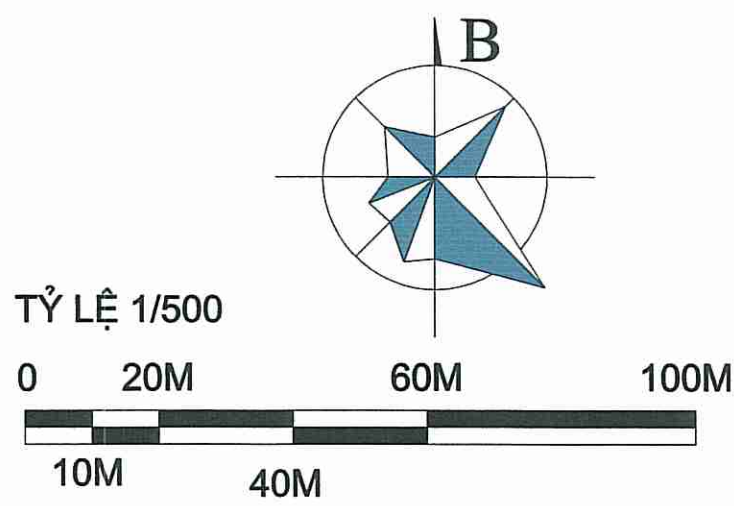

KÝ HIỆU:


- RANH GIỚI LẬP QUY HOẠCH
- ĐẤT CÔNG CỘNG
- ĐẤT Ở TÁI ĐỊNH CƯ
- ĐẤT Ở LIÊN KẾ
- ĐẤT CÂY XANH VƯỜN HOA
- ĐẤT HẠ TẦNG KỸ THUẬT
- ĐƯỜNG GIAO THÔNG
- MẶT CẮT GIAO THÔNG
- TỌA ĐỘ MỐC RANH GIỚI

CHÚ THÍCH:

(A) 100 (m2)

A: THỨ TỰ THỪA ĐẤT

S: DIỆN TÍCH THỪA ĐẤT (M2)

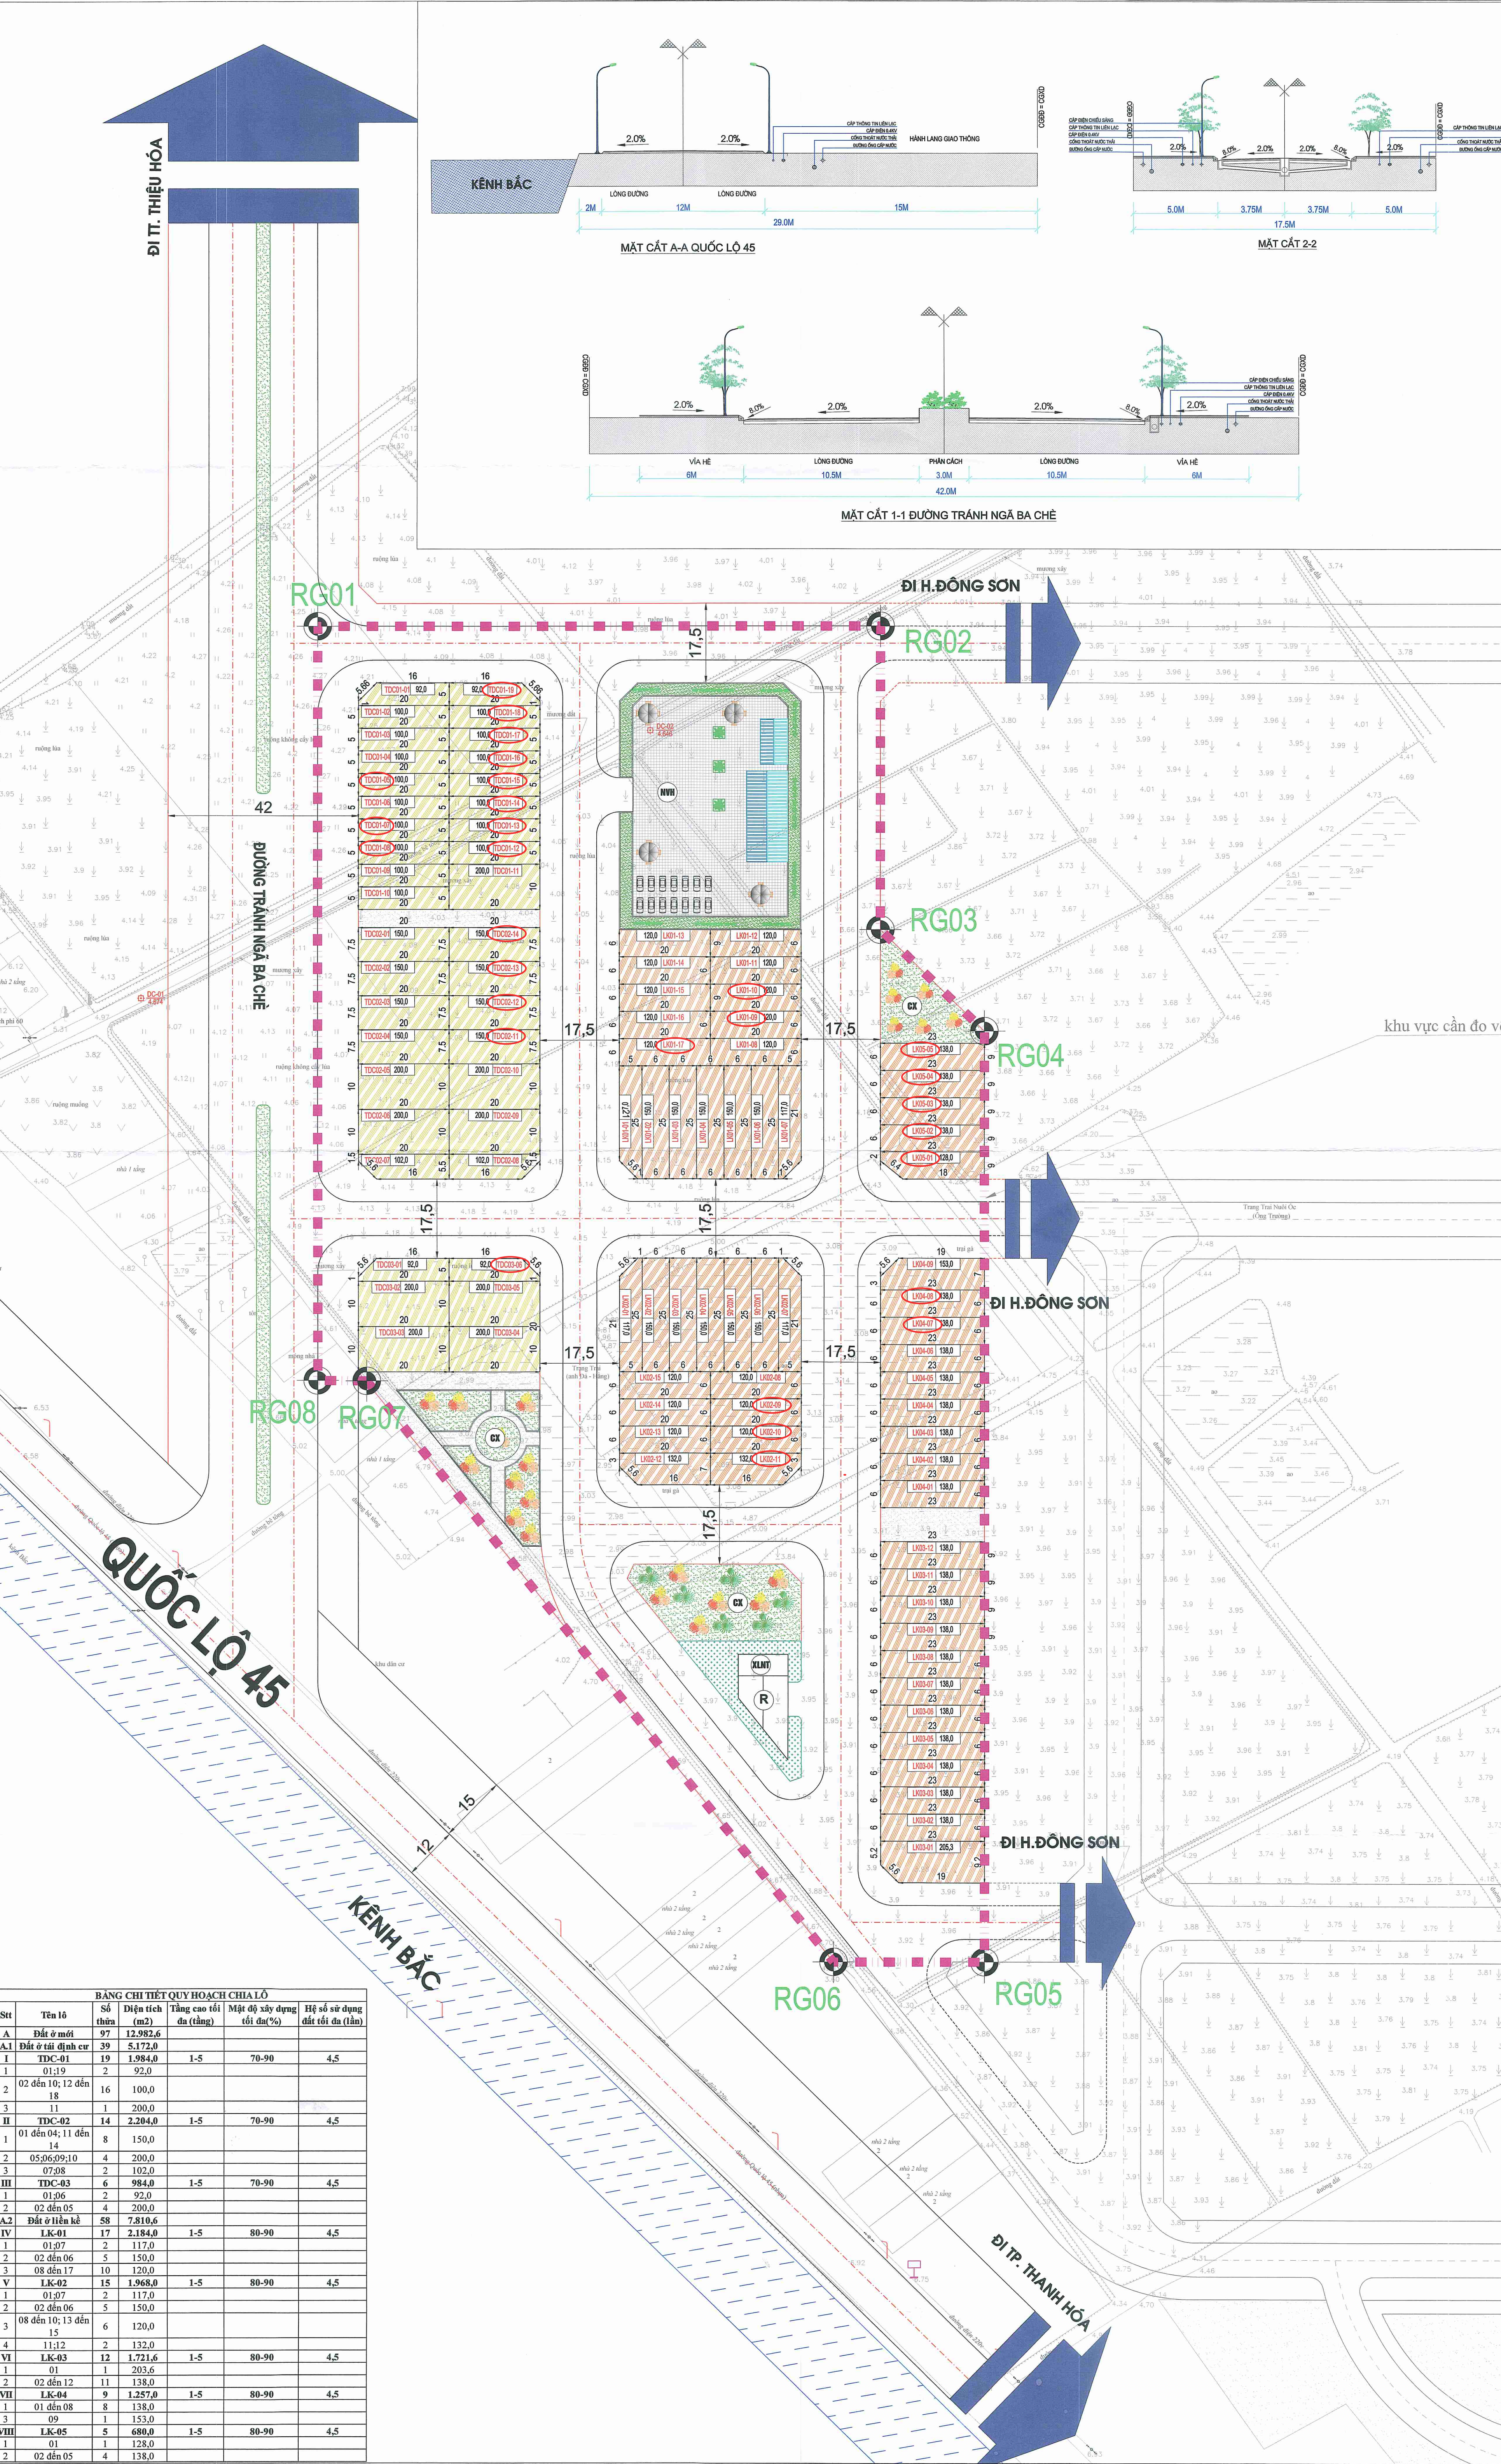

BẢNG CHI TIẾT QUY HOẠCH CHIA LỎ					
Stt	Tên lô	Số thửa	Diện tích (m2)	Tầng cao tối đa (tầng)	Hệ số sử dụng đất tối đa (tần)
A	Đất ở mới	97	12.982,6		
A1	Đất ở tái định cư	39	5.172,0		
I	TĐC-01	19	1.984,0	1-5	70-90
1	01-19	2	92,0		
2	02 đến 10; 12 đến 18	16	100,0		
3	11	1	200,0		
II	TĐC-02	14	2.204,0	1-5	70-90
1	01 đến 04; 11 đến 14	8	150,0		
2	05 đến 09; 10	4	200,0		
3	07-08	2	102,0		
III	TĐC-03	6	984,0	1-5	70-90
1	01-06	2	92,0		
2	02 đến 05	4	200,0		
A2	Đất ở liên kết	58	7.810,6		
IV	LK-01	17	2.184,0	1-5	80-90
1	01-07	2	117,0		
2	02 đến 06	5	150,0		
3	08 đến 17	10	120,0		
V	LK-02	15	1.968,0	1-5	80-90
1	01-07	2	117,0		
2	02 đến 06	5	150,0		
3	08 đến 10; 13 đến 15	6	120,0		
4	11-12	2	132,0		
VI	LK-03	12	1.721,6	1-5	80-90
1	01	1	203,6		
2	02 đến 12	11	138,0		
VII	LK-04	9	1.257,0	1-5	80-90
1	01 đến 08	8	138,0		
3	09	1	153,0		
VIII	LK-05	5	680,0	1-5	80-90
1	01	1	138,0		
2	02 đến 05	4	138,0		

CƠ QUAN PHÊ DUYỆT:
ỦY BAN NHÂN DÂN HUYỆN THIỆU HÓA
KÈM THEO QUYẾT ĐỊNH SỐ: 3807/QĐ-UBND NGÀY 11 THÁNG 9 NĂM 2023

CƠ QUAN THẨM ĐỊNH:
PHÒNG KINH TẾ HẠ TẦNG HUYỆN THIỆU HÓA
KÈM THEO BÁO CÁO THẨM ĐỊNH SỐ: 432/BCTH-TĐ NGÀY 08 THÁNG 9 NĂM 2023

CHỦ ĐẦU TƯ:
BAN QUẢN LÝ DỰ ÁN ĐẦU TƯ VÀ XÂY DỰNG HUYỆN THIỆU HÓA
KÈM THEO TỜ TRÌNH SỐ: 2530/TTR-BQLA NGÀY 08 THÁNG 9 NĂM 2023

TÊN BẢN ÁN:
QUY HOẠCH CHI TIẾT XÂY DỰNG TỈ LỆ 1/500 HẠ TẦNG KỸ THUẬT KHU DÂN CƯ, TÁI ĐỊNH CƯ XÃ THIỆU TRUNG, HUYỆN THIỆU HÓA

TÊN BẢN VẼ:
SƠ ĐỒ TỔ CHỨC KHÔNG GIAN KIẾN TRÚC CẢNH QUAN

BẢN VẼ: QH-04
THIẾT KẾ: KS. ĐỖ ANH TUẤN
CHỦ TRÌ: KTS. NGUYỄN ANH CHIẾN
CHỦ NHIỆM: KTS. NGUYỄN ANH CHIẾN
TRƯỞNG PHÒNG: KTS. NGUYỄN ANH CHIẾN
QL. KỸ THUẬT: KS. TRƯƠNG THỊ BÍCH HẢO

GIÁM ĐỐC: BÙI VĂN HỢP
CÔNG TY TNHH TƯ VẤN XÂY DỰNG VINH QUANG
ĐC: 02 NG. 1 X. 01 Đ. 01 P. 01 Q. 01 T. 01

TÊN BẢN ÁN: QUY HOẠCH CHI TIẾT XÂY DỰNG TỈ LỆ 1/500 HẠ TẦNG KỸ THUẬT KHU DÂN CƯ, TÁI ĐỊNH CƯ XÃ THIỆU TRUNG, HUYỆN THIỆU HÓA
TÊN BẢN VẼ: SƠ ĐỒ TỔ CHỨC KHÔNG GIAN KIẾN TRÚC CẢNH QUAN

